

Seal:

DATE: 2022.04.21

Owner:



AUGMENTECH EDUCATION PVT. LTD.
augmotech@gmail.com
<https://www.augmotech.com/>
JAMSHEDPUR, INDIA-832110

25 FLOORS OFFICE BUILDING

WEST HIGH COURT ROAD
MICHIGAN, USA

ISSUE NO.	DELTA	ISSUE DATE	DESCRIPTION
1	1	2022.04.30	ISSUED FOR PERMIT

CURRENT ISSUE

ISSUED FOR PERMIT

CURRENT ISSUE DATE
2022.04.30

DRAWN BY
VR

CHECKED BY
CT

PROJECT NO.
179-64-01

SHEET NAME

3D VIEW OF BASE LEVEL PLAN

DRAWINGS NO.

A100

① 3D VIEW OF BASE LEVEL PLAN



Seal:

DATE: 2022.04.21

Owner:



AUGMENTECH EDUCATION PVT. LTD.
augmotech@gmail.com
<https://www.augmotech.com/>
JAMSHEDPUR, INDIA-832110

25 FLOORS OFFICE BUILDING

WEST HIGH COURT ROAD
MICHIGAN, USA

ISSUE NO.	DELTA	ISSUE DATE	DESCRIPTION
1	1	2022.04.30	ISSUED FOR PERMIT

CURRENT ISSUE

ISSUED FOR PERMIT

CURRENT ISSUE DATE
2022.04.30

DRAWN BY
VR

CHECKED BY
CT


PROJECT NO.
179-64-01

SHEET NAME

3D VIEW OF 1ST LEVEL PLAN

DRAWINGS NO.

A100.1

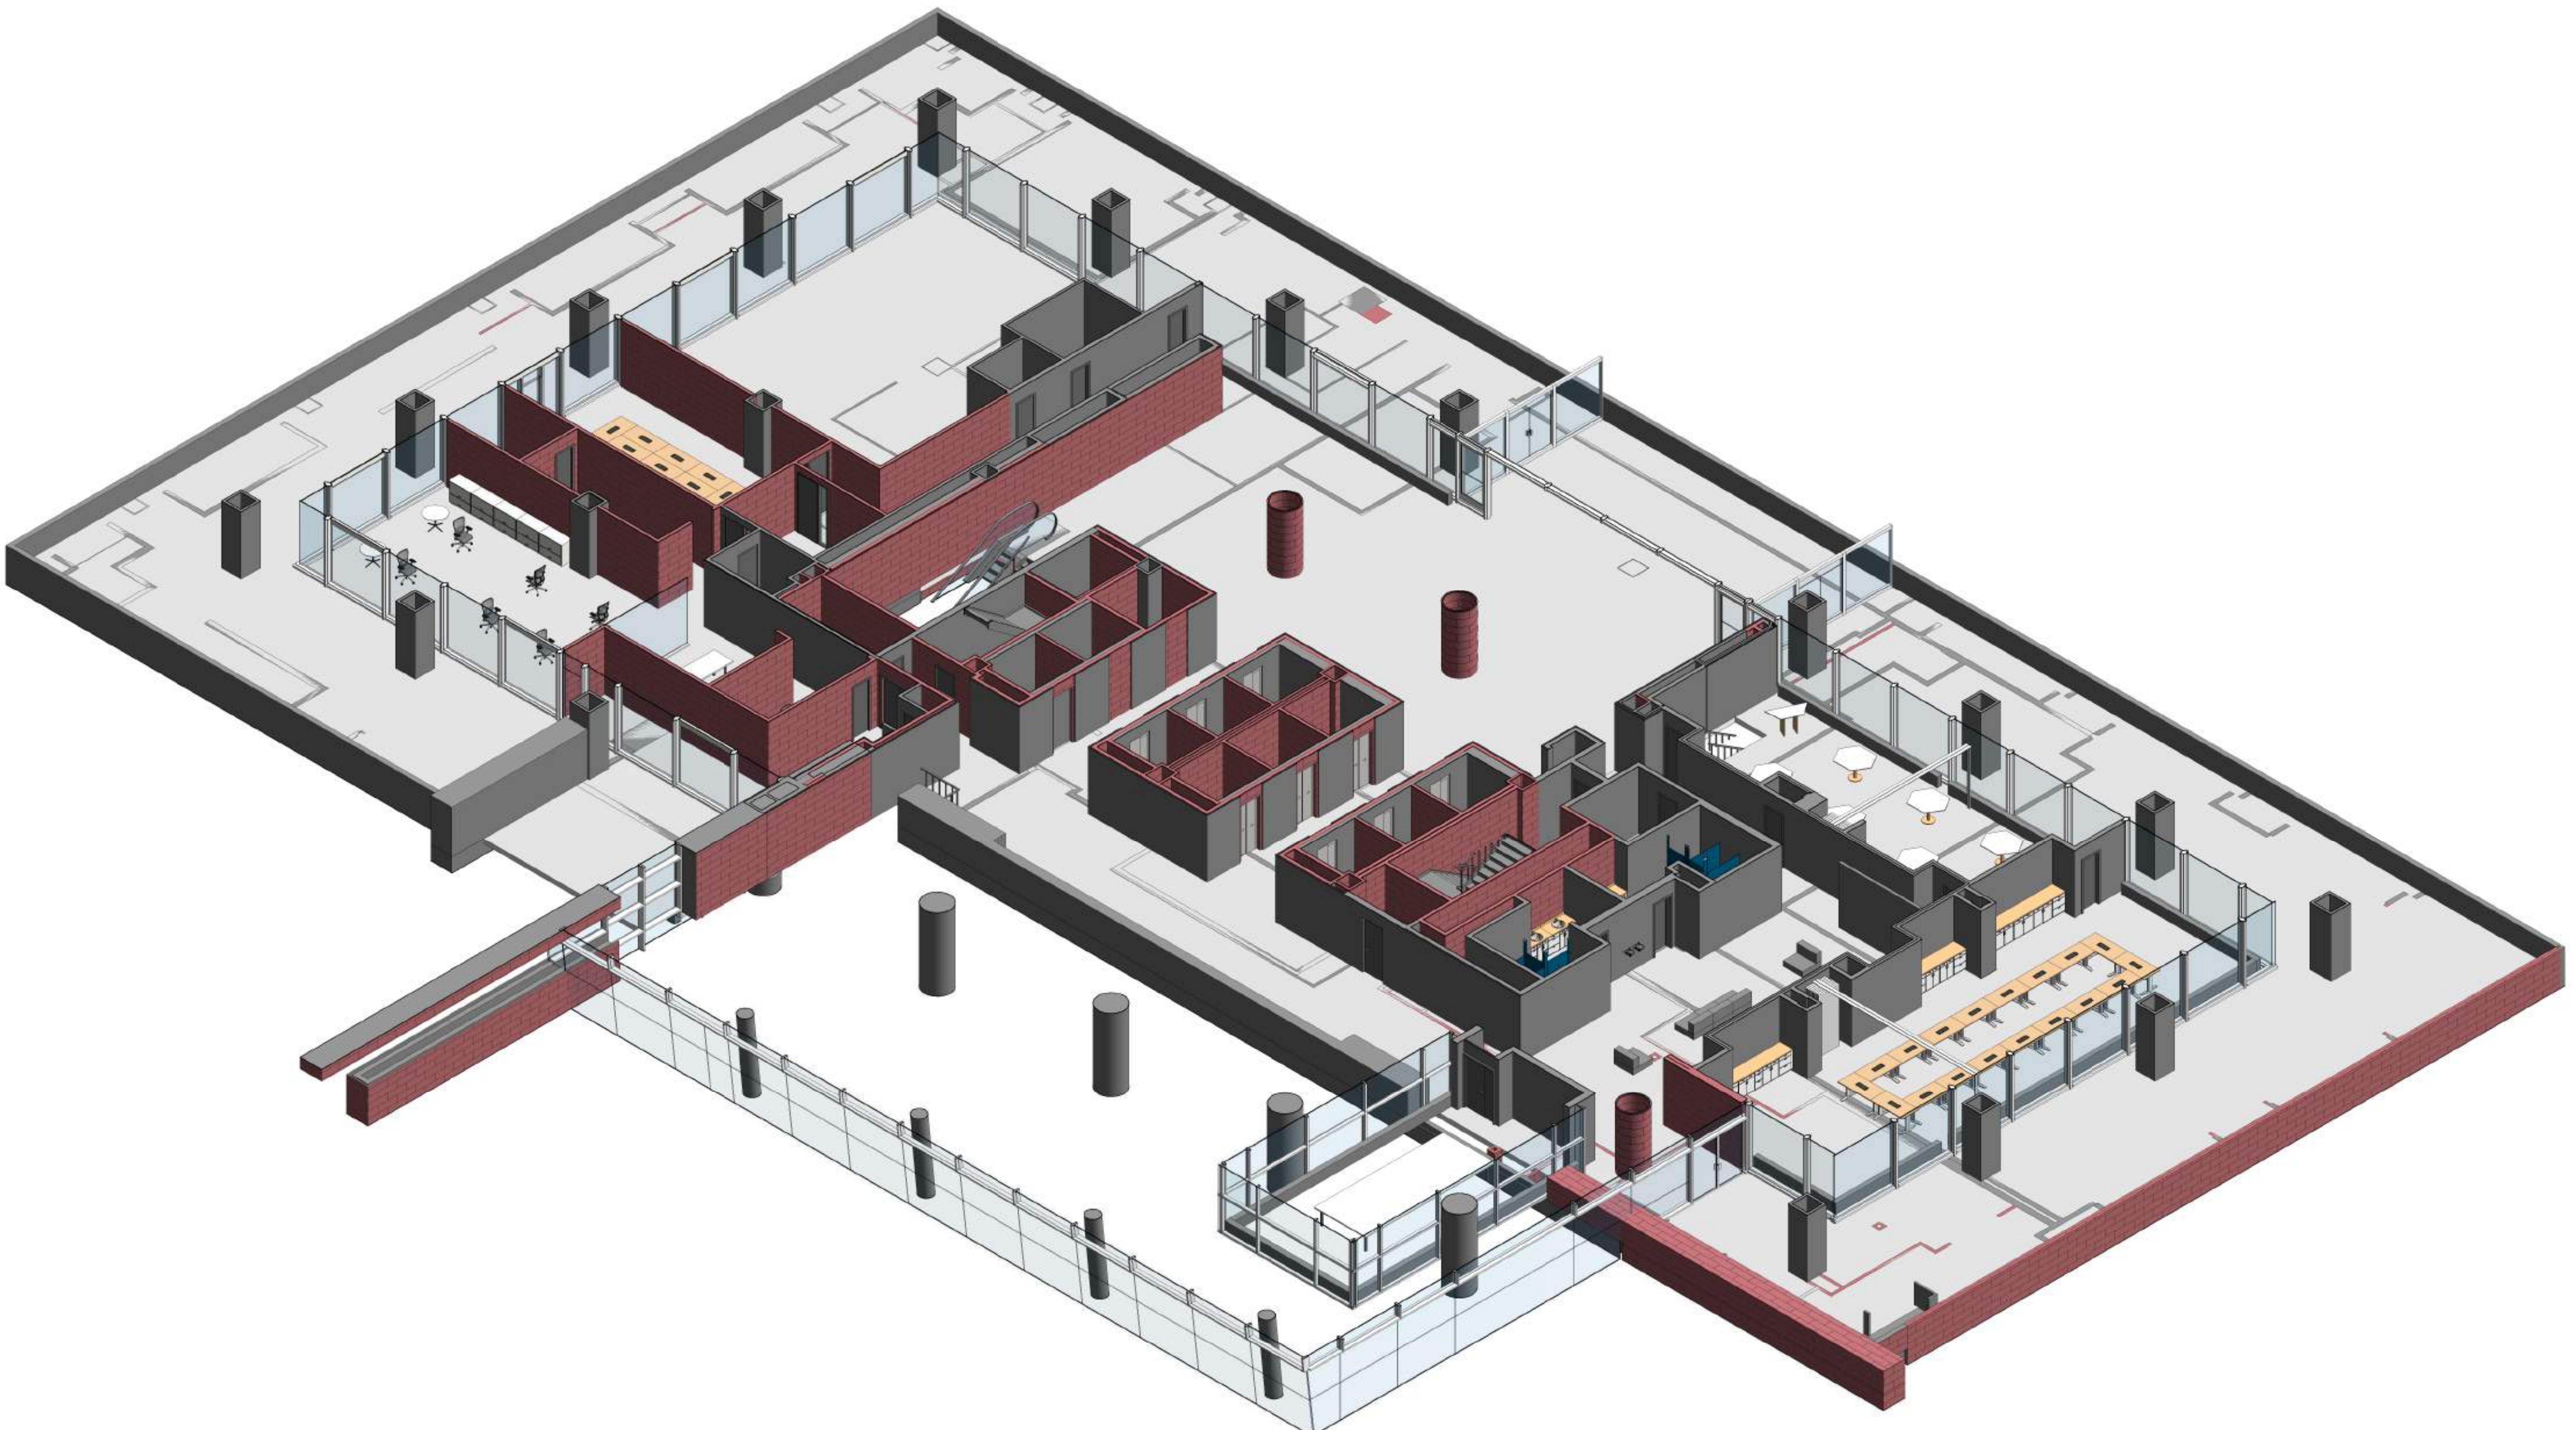

1 3D VIEW OF 1ST LEVEL PLAN

Seal:

DATE: 2022.04.21

Owner:



AUGMENTECH EDUCATION PVT. LTD.
augmotech@gmail.com
<https://www.augmotech.com/>
JAMSHEDPUR, INDIA-832110

25 FLOORS OFFICE BUILDING

WEST HIGH COURT ROAD
MICHIGAN, USA

ISSUE NO.	DELTA	ISSUE DATE	DESCRIPTION
1	1	2022.04.30	ISSUED FOR PERMIT

CURRENT ISSUE

ISSUED FOR PERMIT

CURRENT ISSUE DATE
2022.04.30

DRAWN BY
VR

CHECKED BY
CT

PROJECT NO.
179-64-01


SHEET NAME

3D VIEW OF TYPICAL LEVEL PLAN

DRAWINGS NO.

A100.2

1 3D VIEW OF TYPICAL LEVEL PLAN

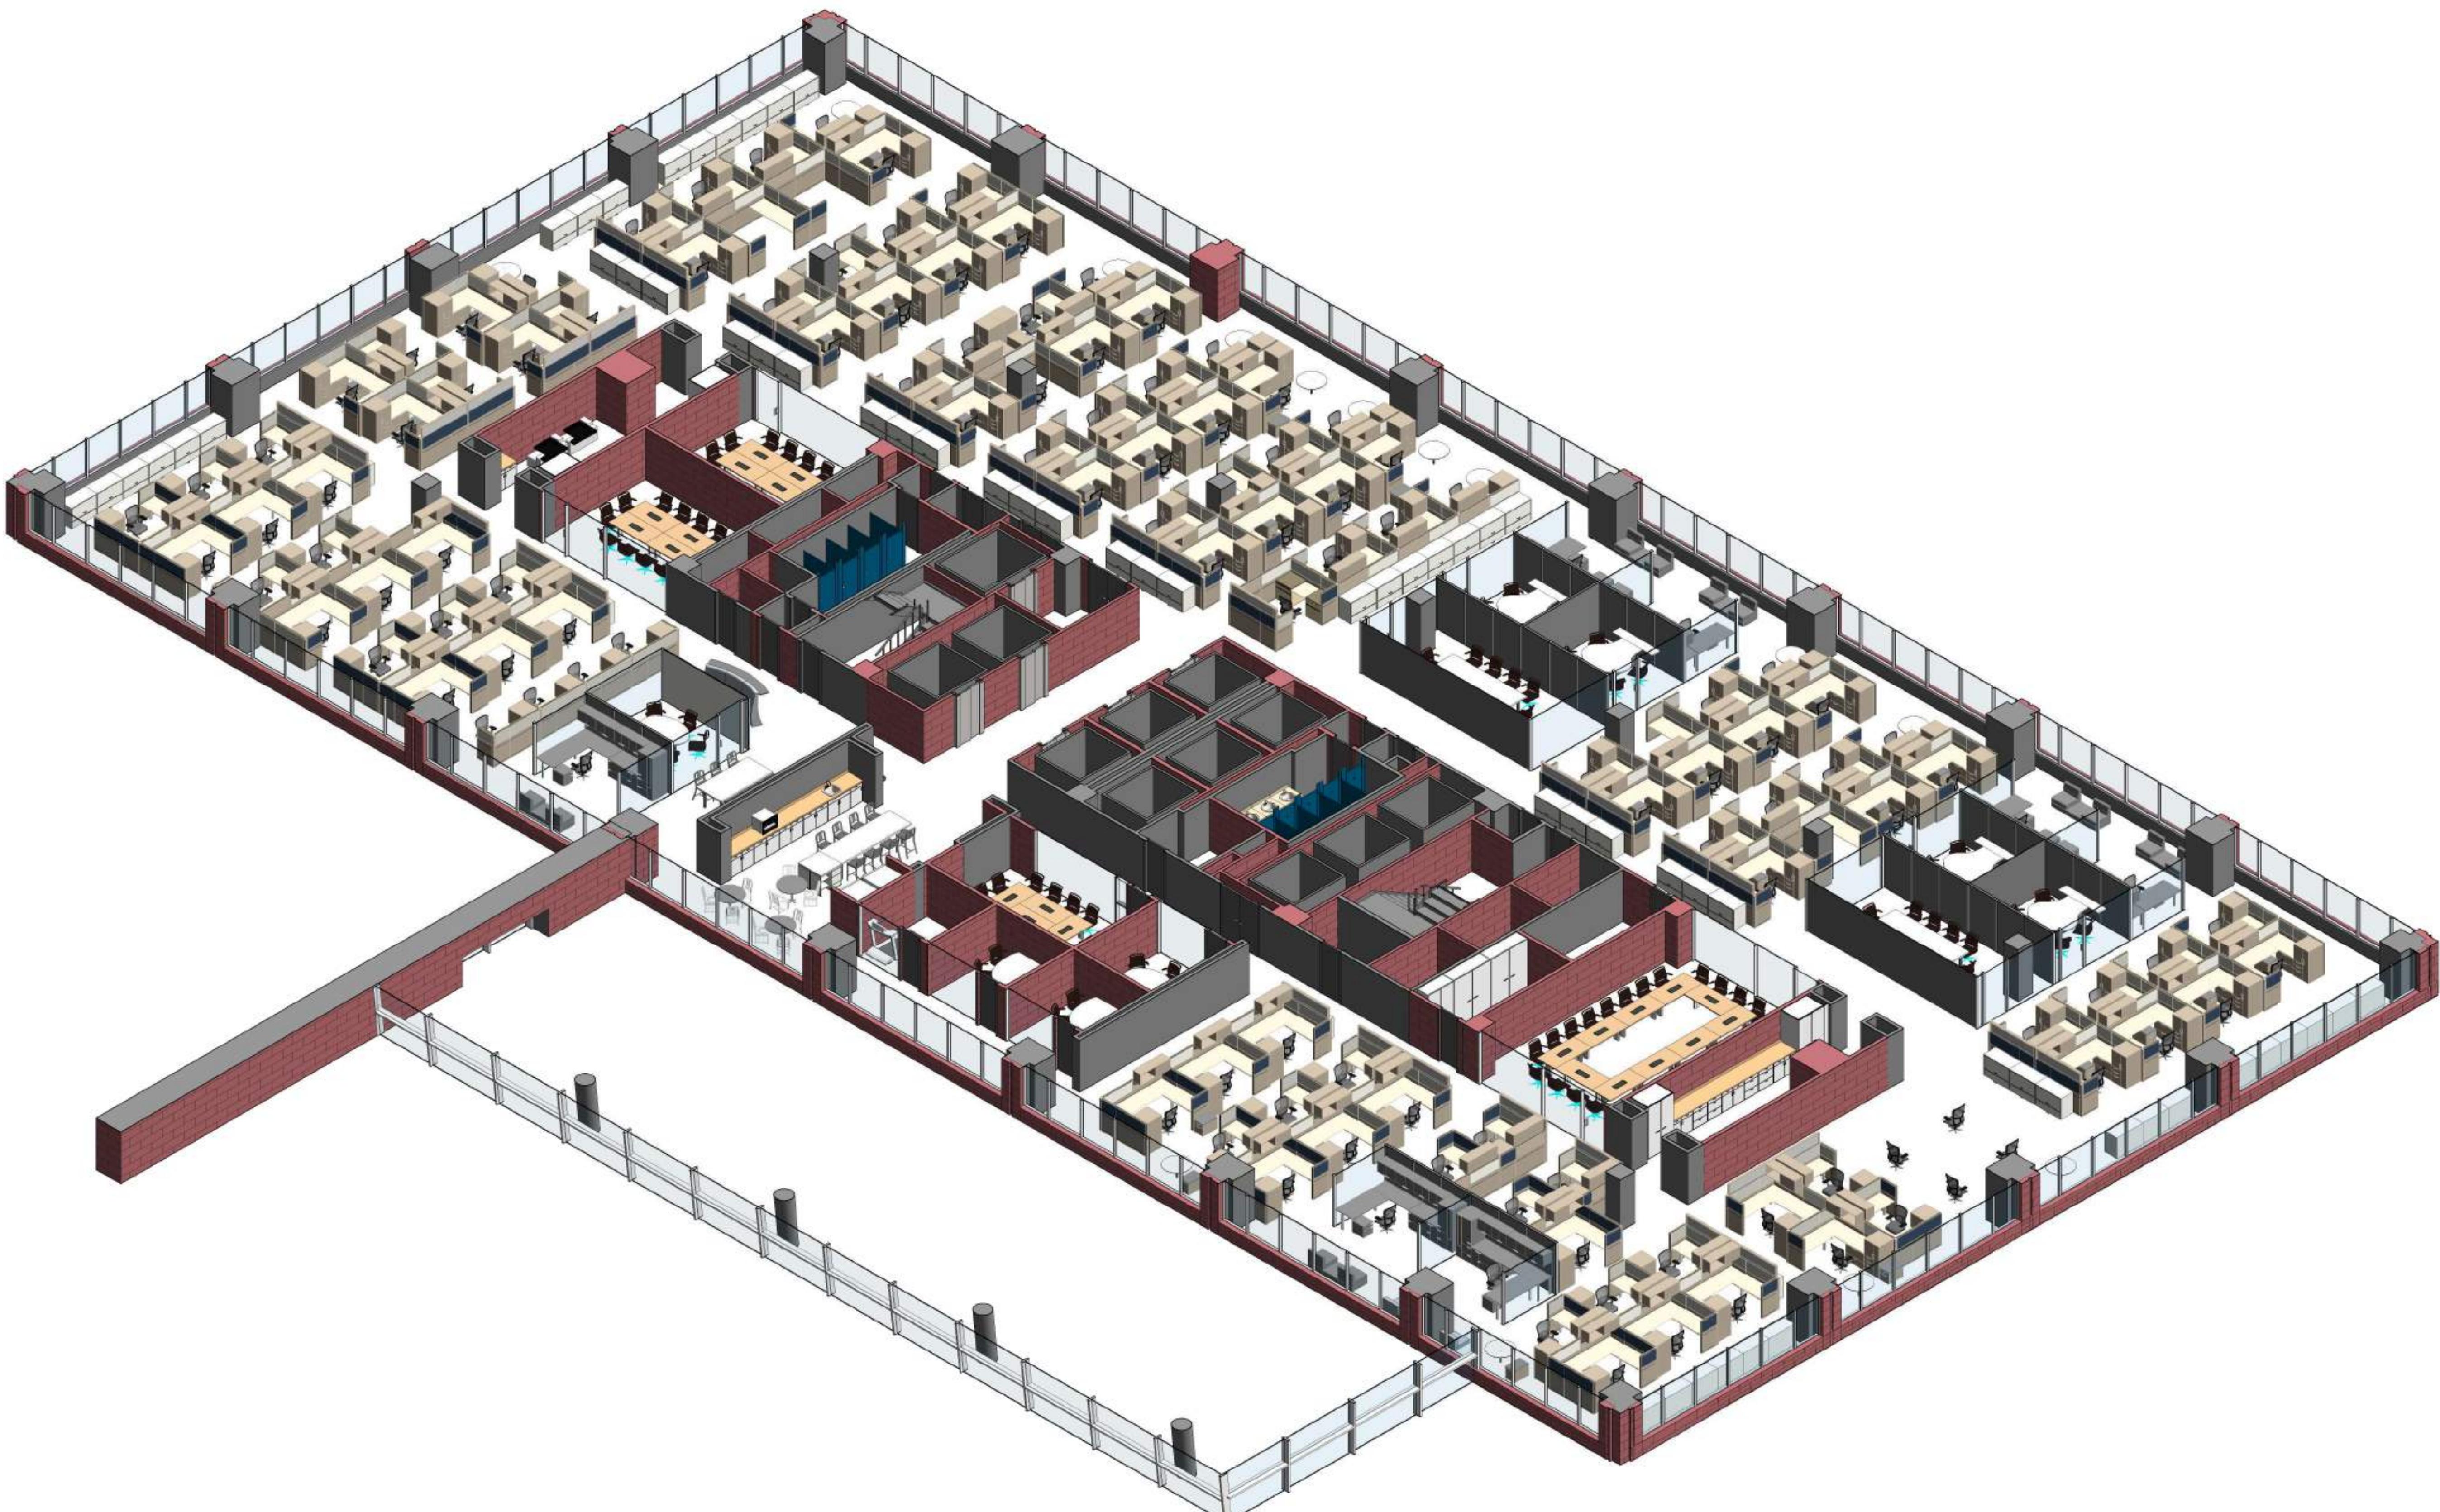

Seal:

DATE: 2022.04.21

Owner:



AUGMENTECH EDUCATION PVT. LTD.
augmintechn@gmail.com
<https://www.augmintechn.com/>
JAMSHEDPUR, INDIA-832110

25 FLOORS OFFICE BUILDING

WEST HIGH COURT ROAD
MICHIGAN, USA

ISSUE NO.	DELTA	ISSUE DATE	DESCRIPTION
1	1	2022.04.30	ISSUED FOR PERMIT

CURRENT ISSUE

ISSUED FOR PERMIT

CURRENT ISSUE DATE
2022.04.30

DRAWN BY
VR

CHECKED BY
CT


PROJECT NO.
179-64-01

SHEET NAME

3D VIEW OF 25TH FLOOR OFFICE BUILDING

DRAWINGS NO.

A100.3

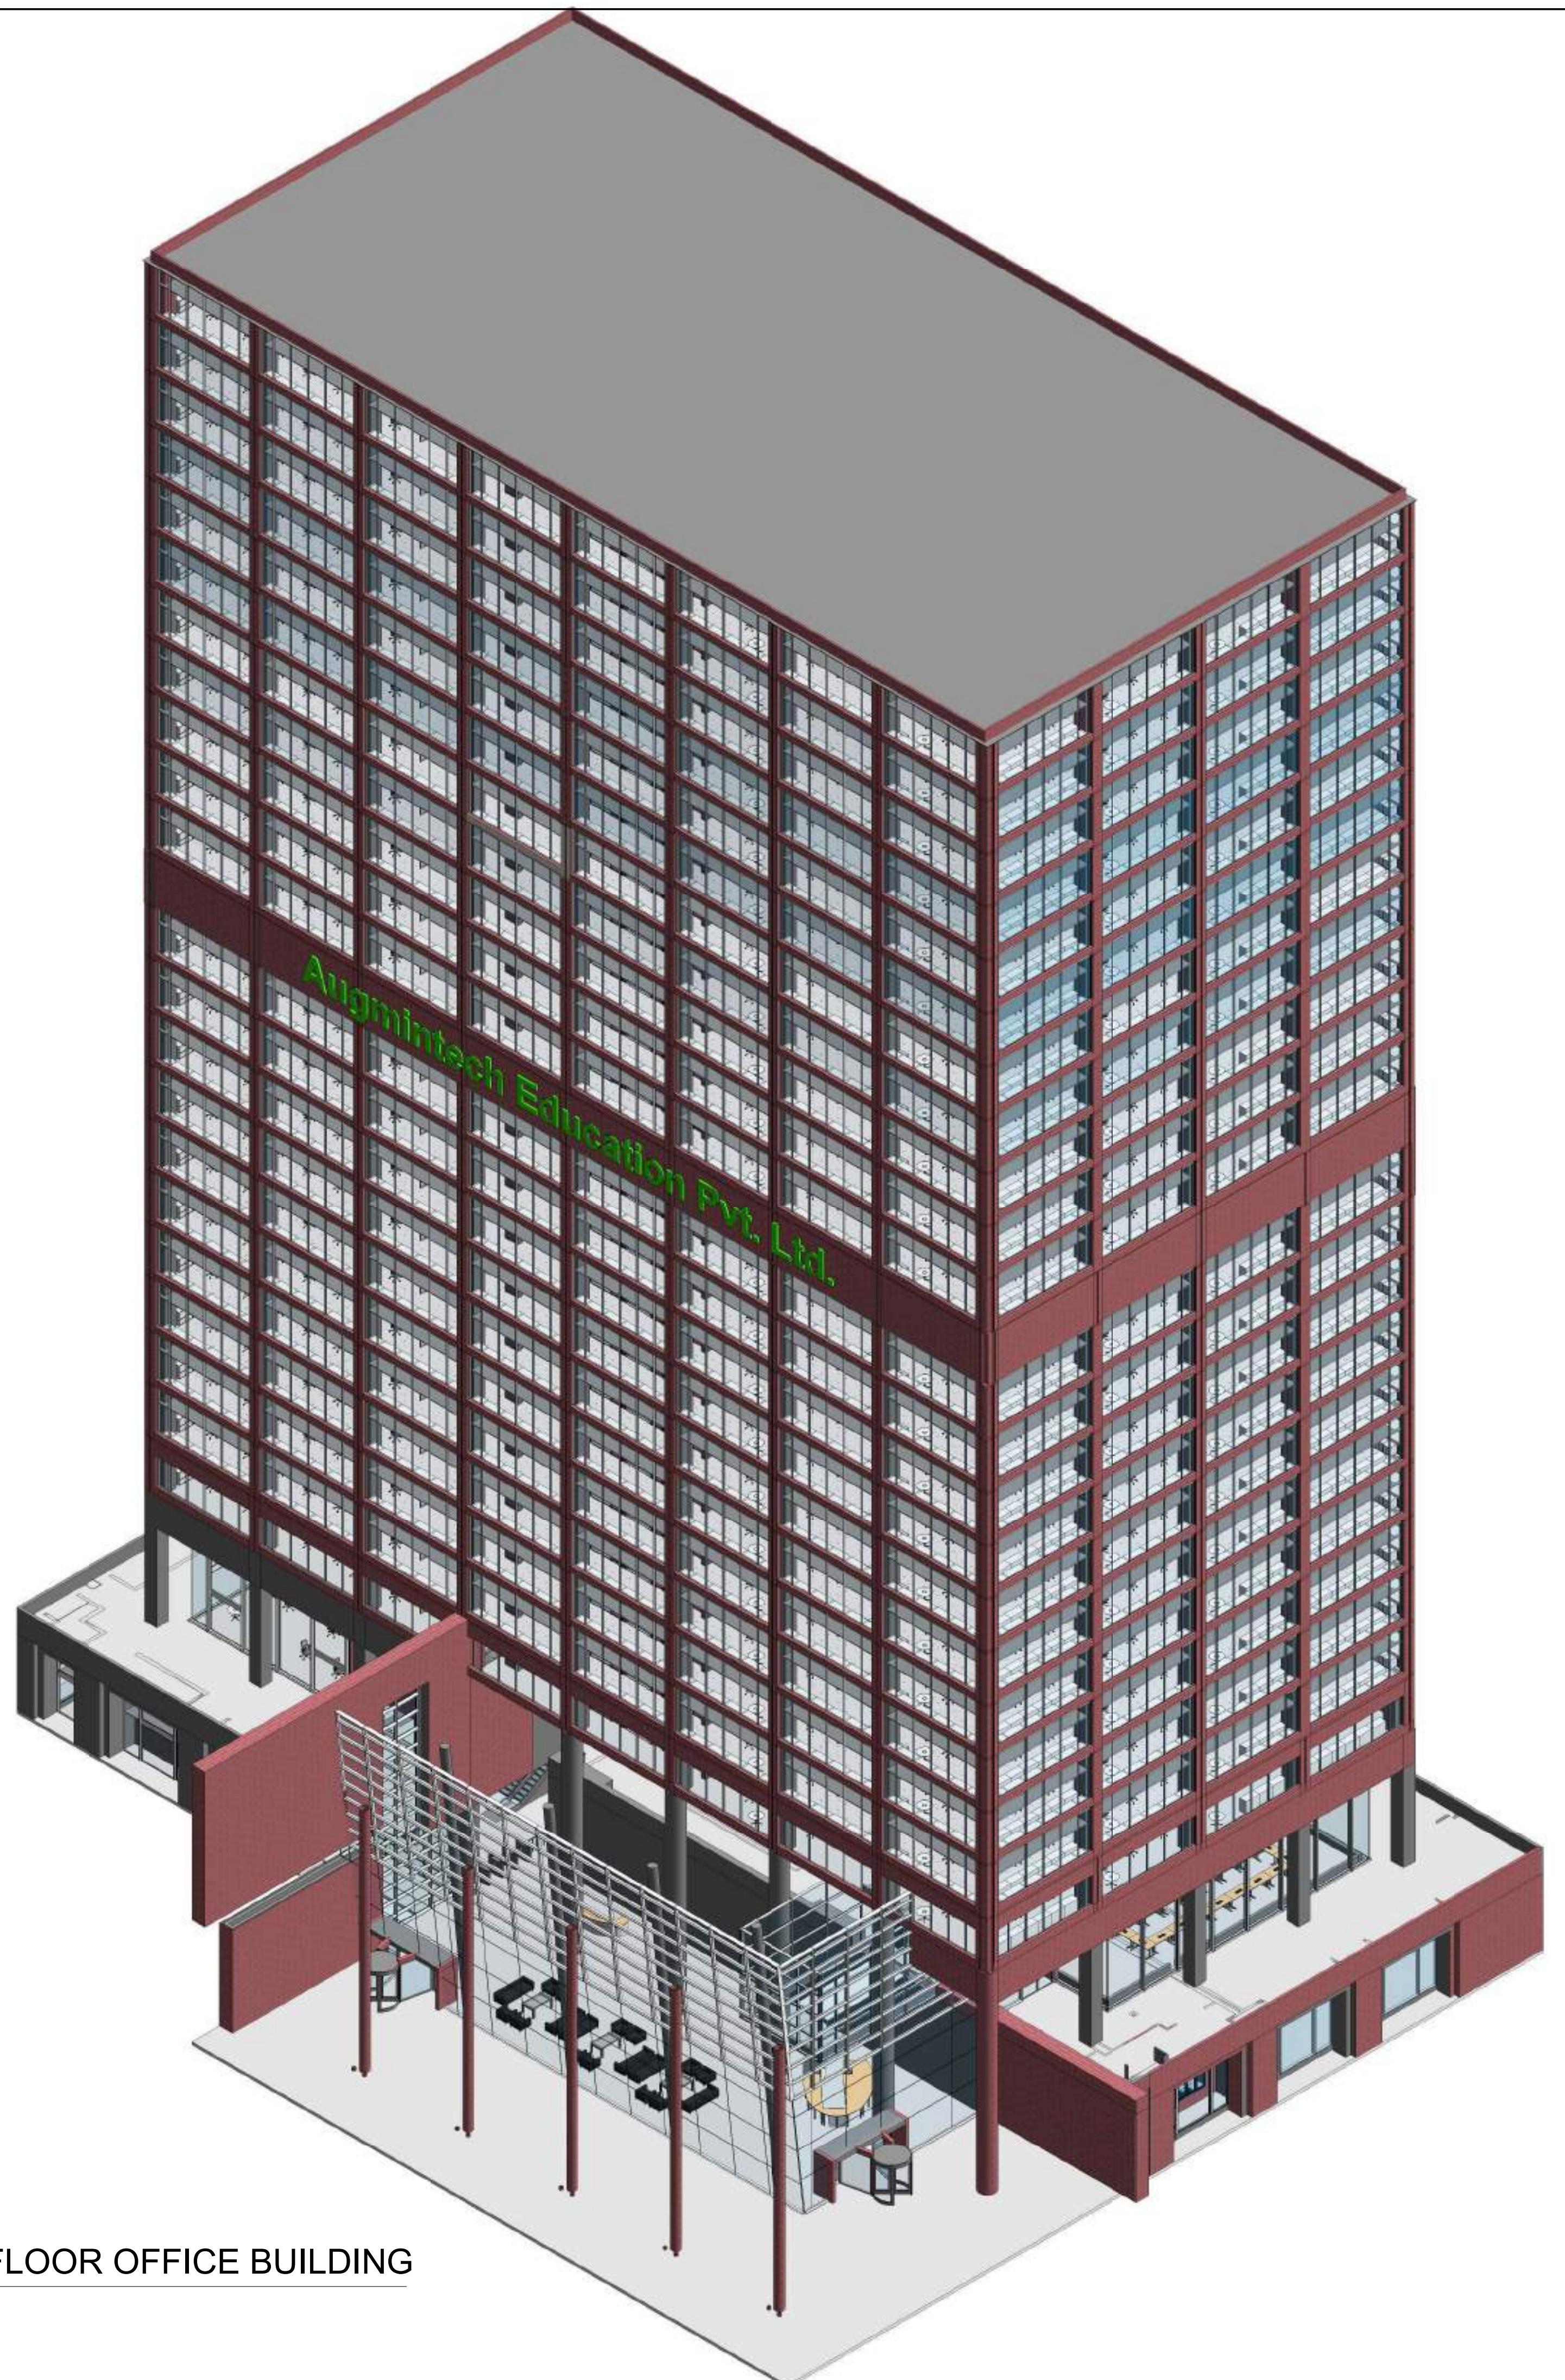

3D VIEW OF 25TH FLOOR OFFICE BUILDING

1

Seal:

DATE: 2022.04.21

Owner:



AUGMENTECH EDUCATION PVT. LTD.
augmotech@gmail.com
<https://www.augmotech.com/>
JAMSHEDPUR, INDIA-832110

25 FLOORS OFFICE BUILDING

WEST HIGH COURT ROAD
MICHIGAN, USA

ISSUE NO.	DELTA	ISSUE DATE	DESCRIPTION
1	1	2022.04.30	ISSUED FOR PERMIT

CURRENT ISSUE

ISSUED FOR PERMIT

CURRENT ISSUE DATE
2022.04.30

DRAWN BY

VR

CHECKED BY

CT


PROJECT NO.

179-64-01

SHEET NAME

Base Level Floor Plan

DRAWINGS NO.

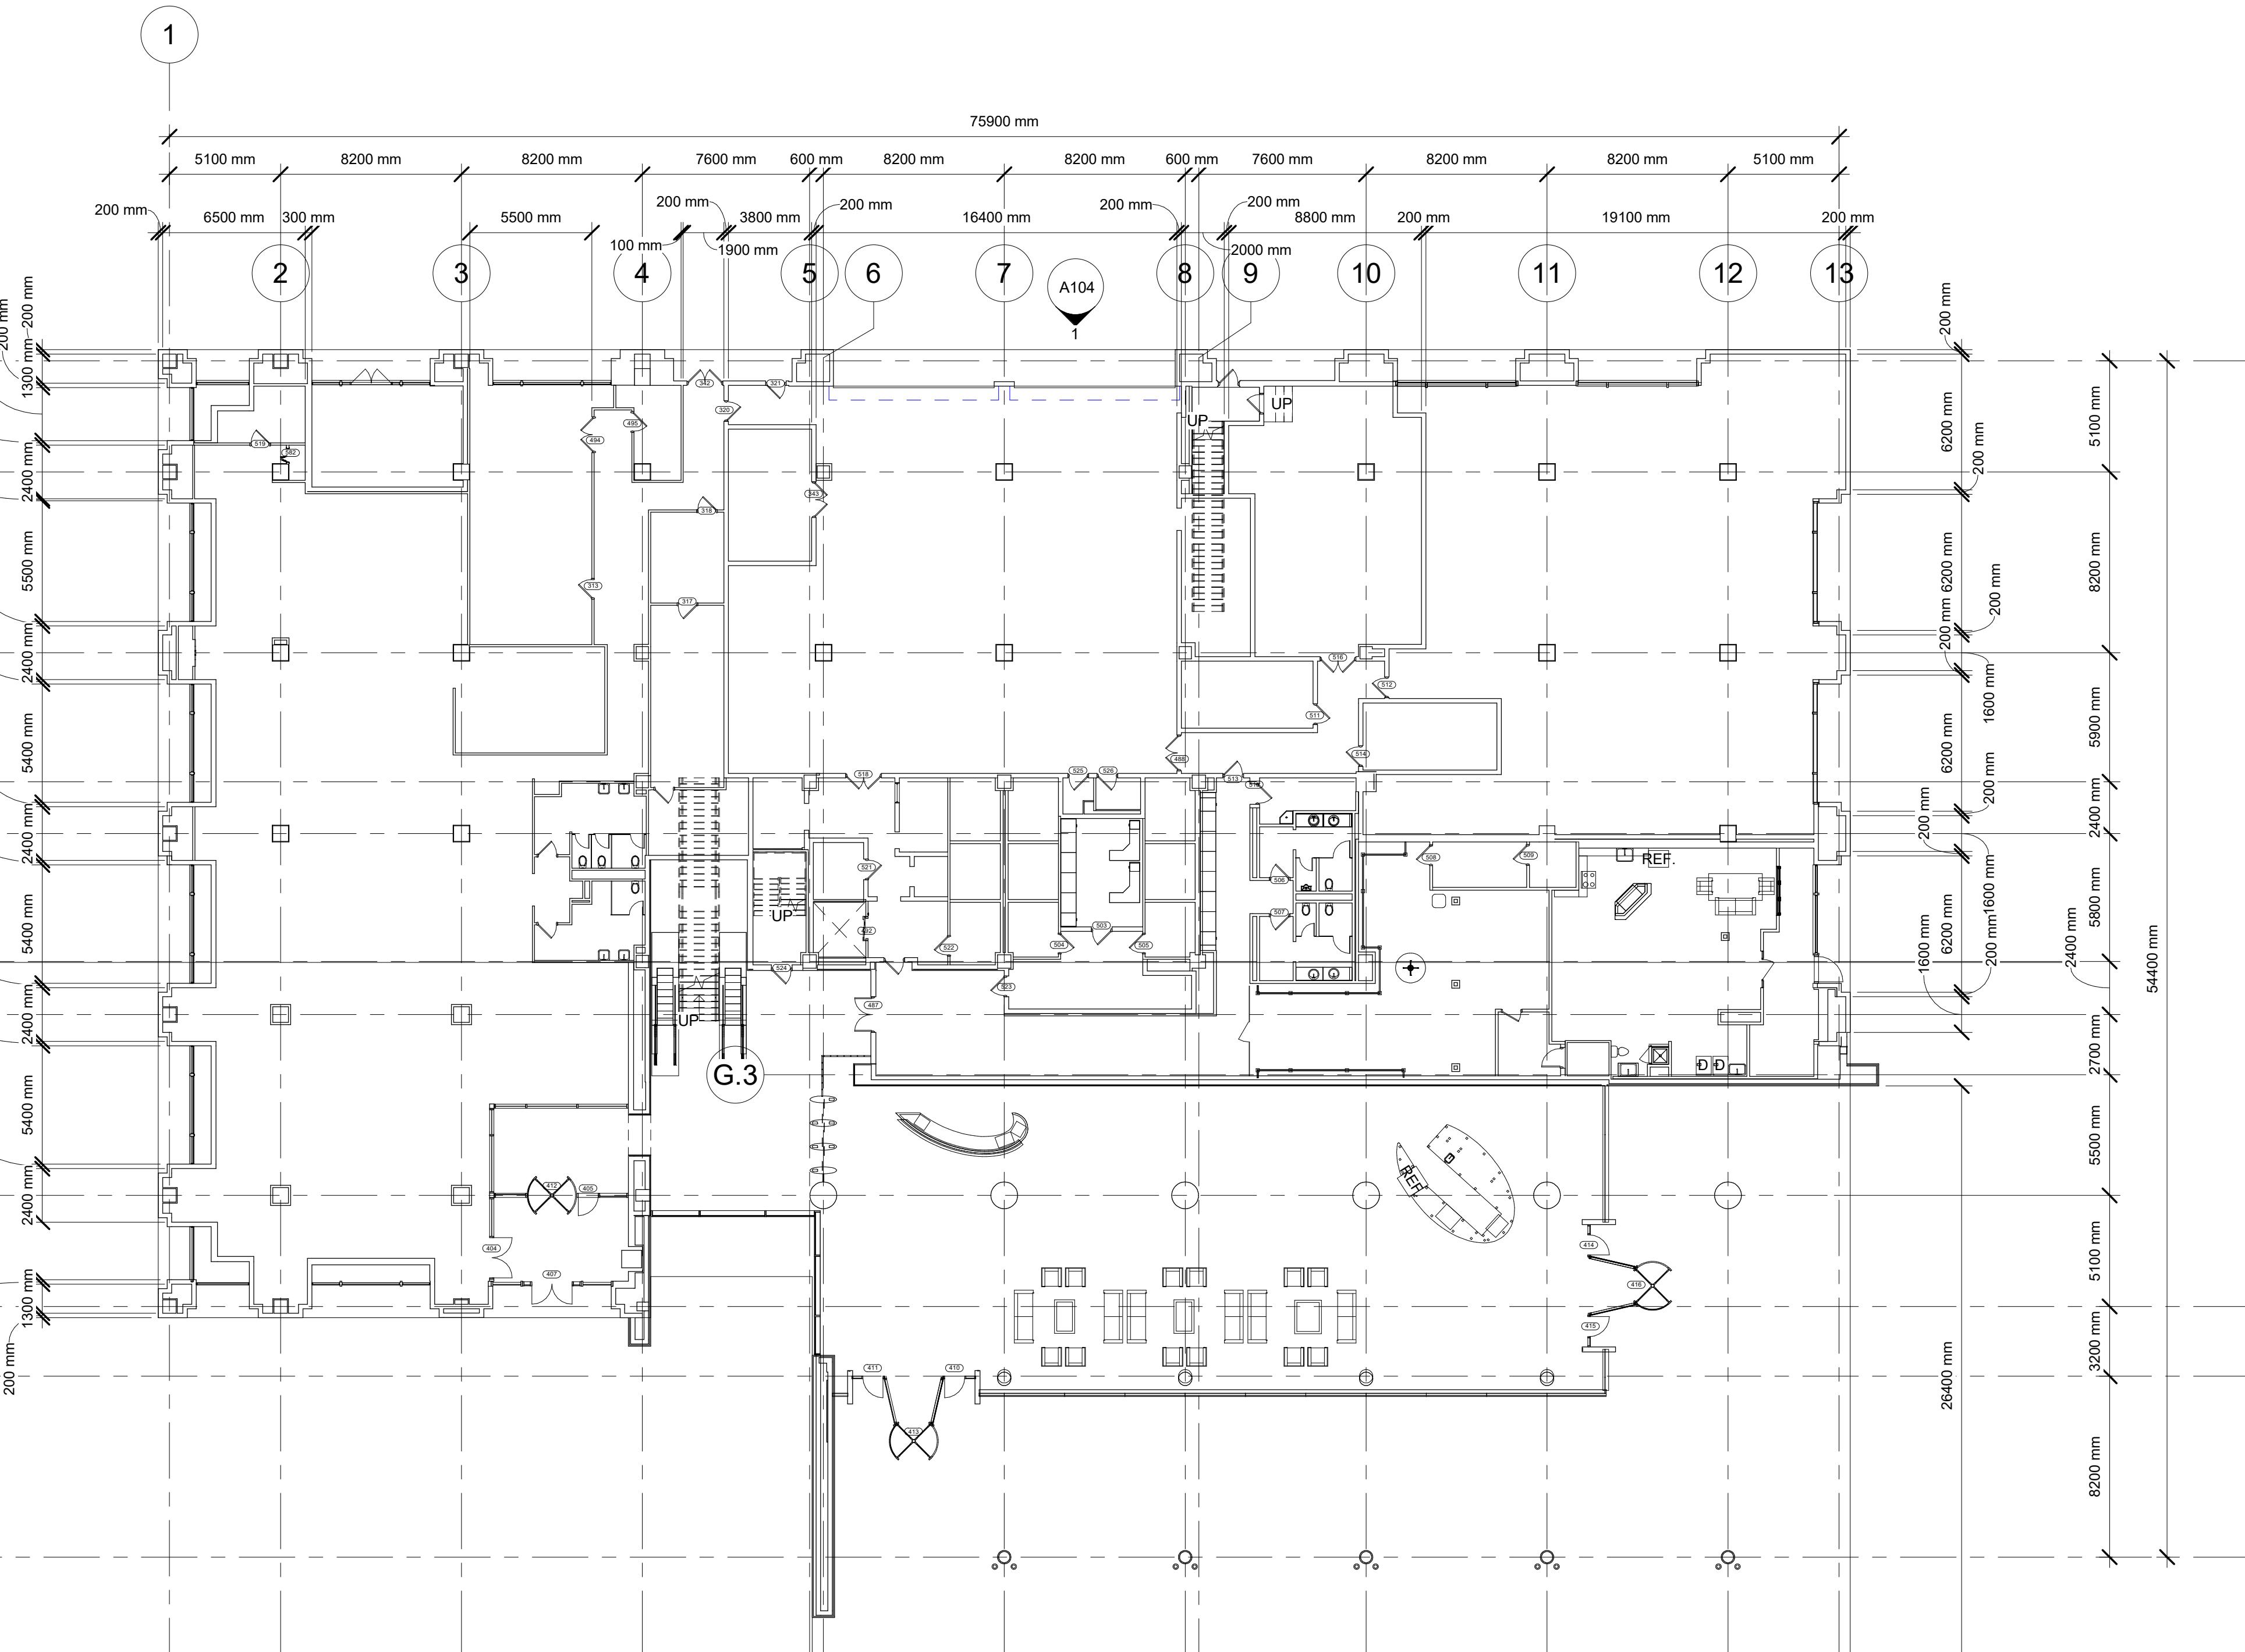A101

1 Base Level
1 : 200

Seal:

DATE: 2022.04.21

Owner:



AUGMENTECH EDUCATION PVT. LTD.
augmtech@gmail.com
<https://www.augmtech.com/JAMSHEDPUR, INDIA-832110>

25 FLOORS OFFICE BUILDING

WEST HIGH COURT ROAD
MICHIGAN, USA

ISSUE NO.	DELTA	ISSUE DATE	DESCRIPTION
1	1	2022.04.30	ISSUED FOR PERMIT

CURRENT ISSUE


ISSUED FOR PERMIT

CURRENT ISSUE DATE
2022.04.30DRAWN BY
VRCHECKED BY
CTPROJECT NO.
179-64-01

SHEET NAME

TYPICAL FLOOR PLAN

DRAWINGS NO.

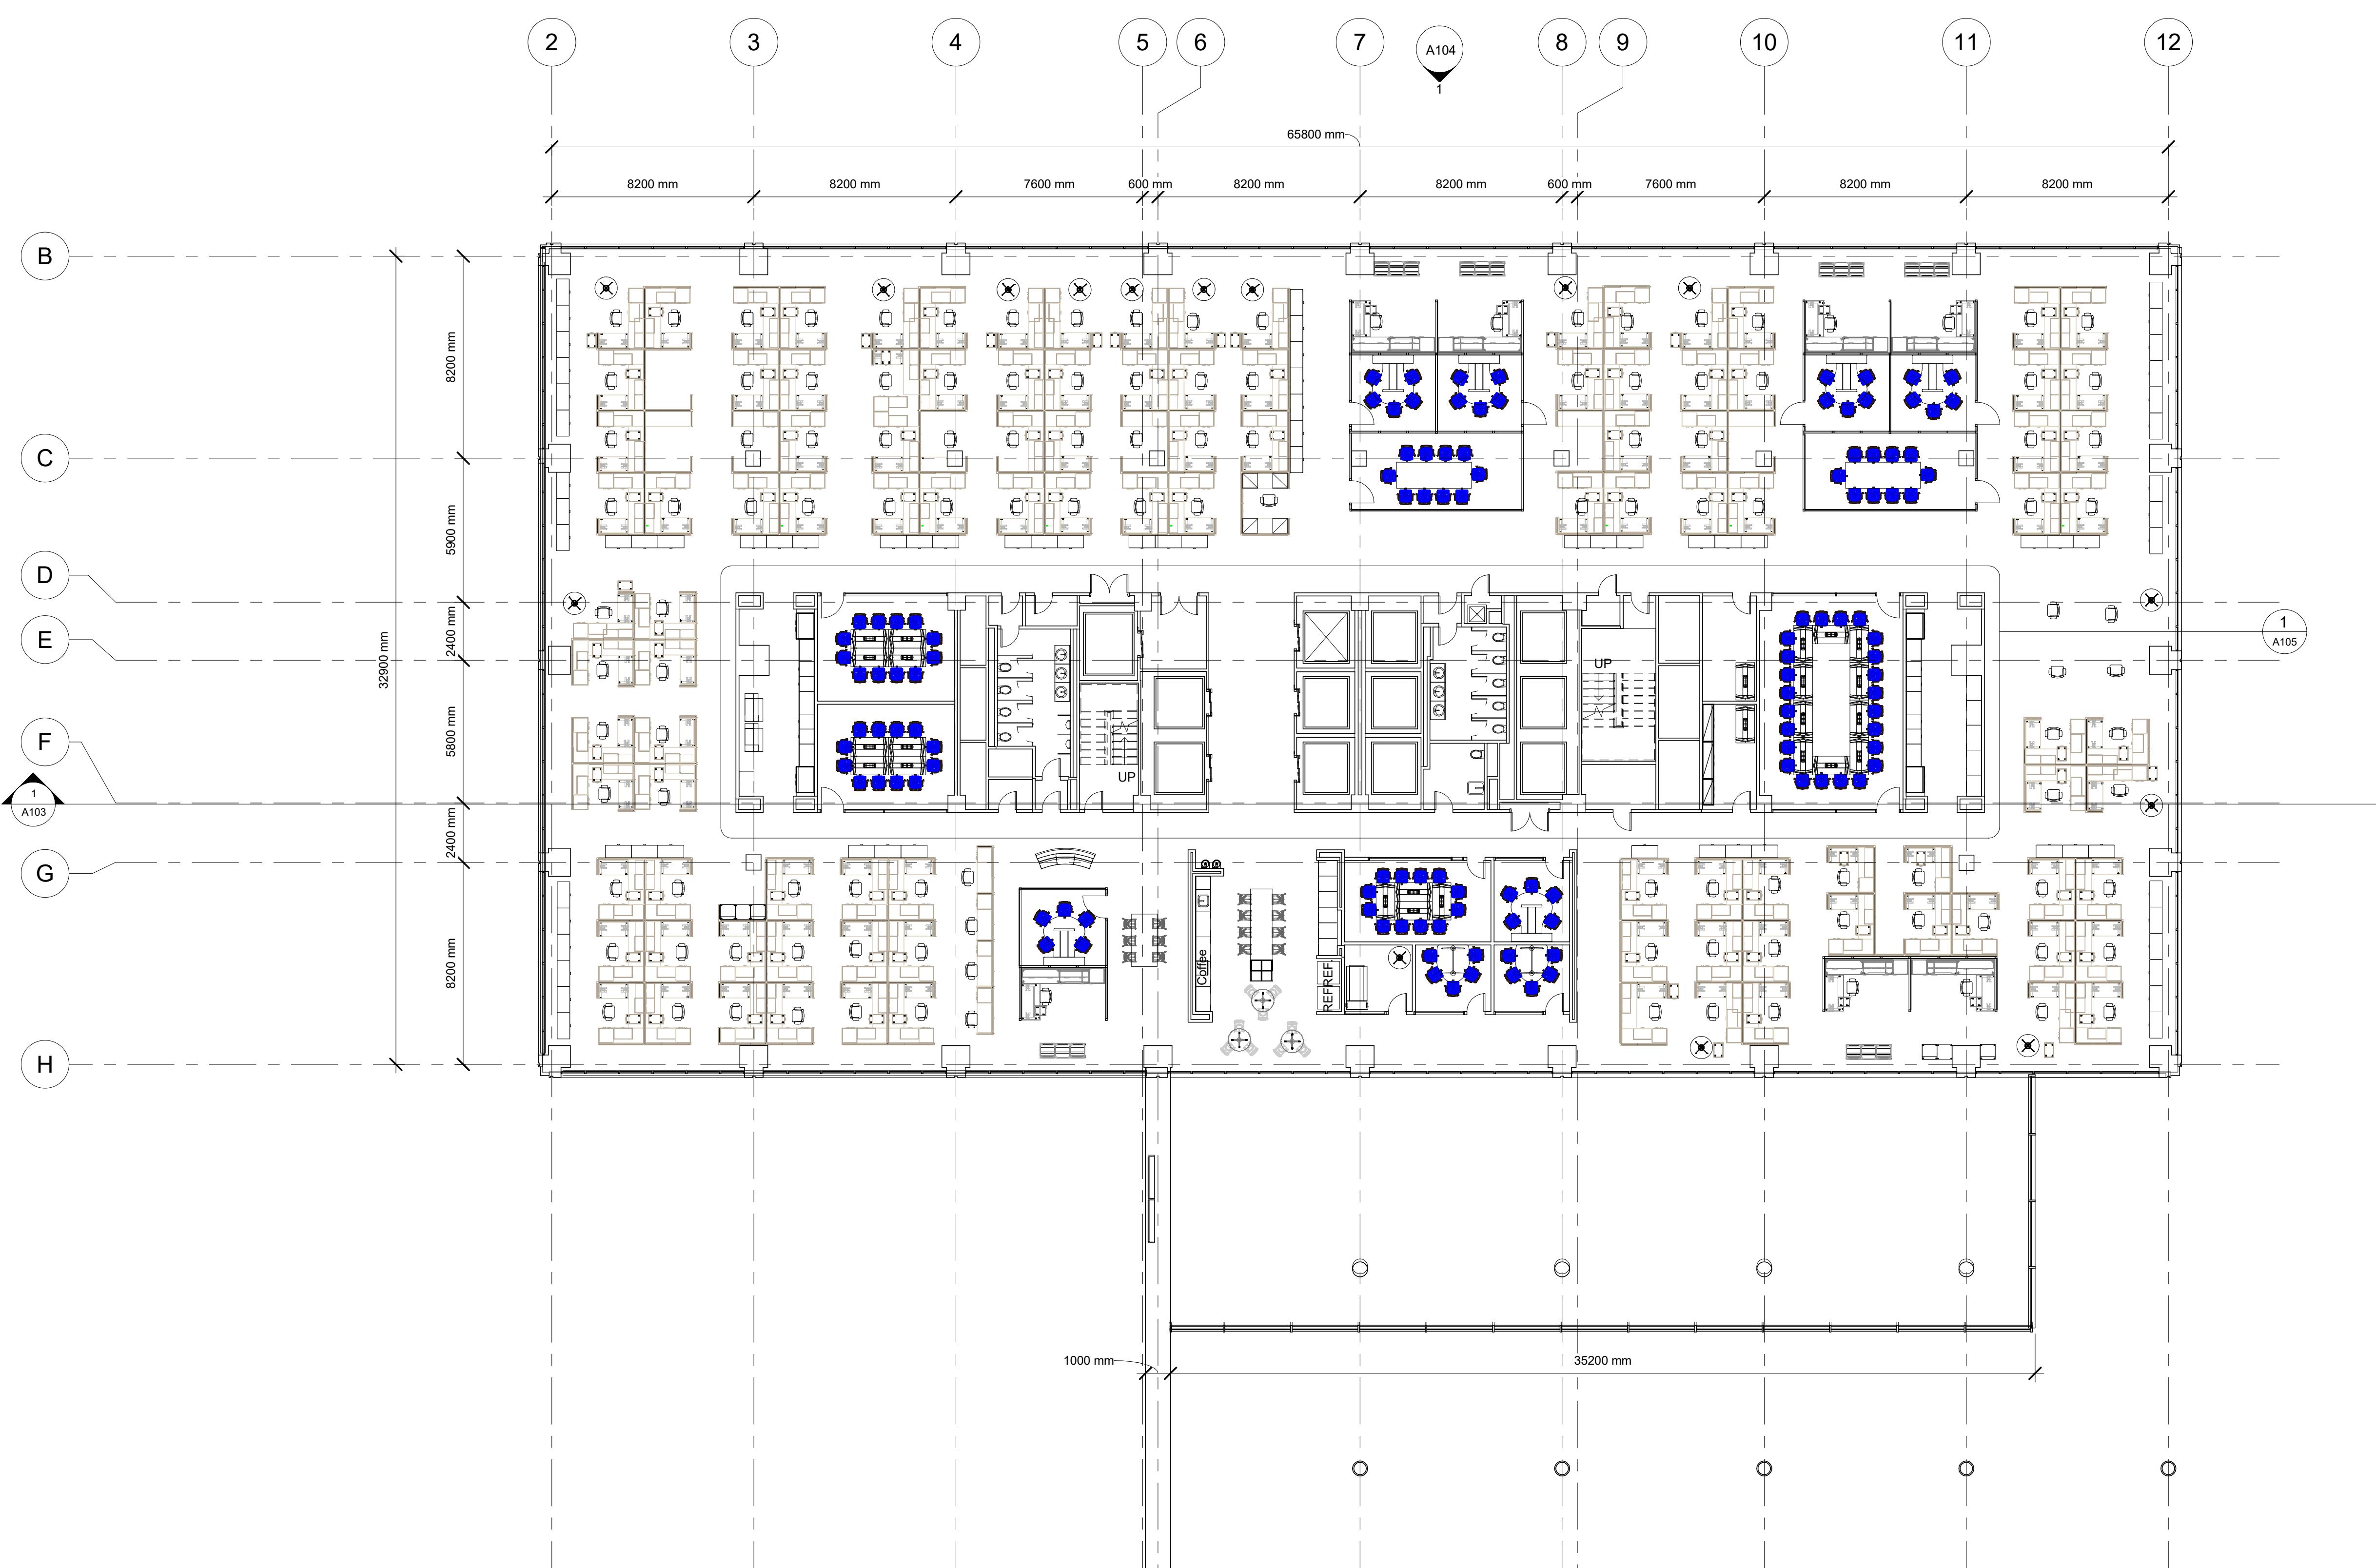A102

1 TYPICAL LEVEL FLOOR PLAN

1 : 150



DRAWINGS NO.

A103

Seal:

DATE: 2022.04.21

Owner:



AUGMENTECH EDUCATION PVT. LTD.
augmotech@gmail.com
<https://www.augmotech.com/>
JAMSHEDPUR, INDIA-832110

25 FLOORS OFFICE BUILDING

WEST HIGH COURT ROAD
MICHIGAN, USA

ISSUE NO.	DELTA	ISSUE DATE	DESCRIPTION
1	1	2022.04.30	ISSUED FOR PERMIT

CURRENT ISSUE

ISSUED FOR PERMIT

CURRENT ISSUE DATE
2022.04.30
DRAWN BY
Author
CHECKED BY
Checker
PROJECT NO.
179-64-01

SHEET NAME

Building Sectional View

Seal: _____

DATE: 2022.04.21

Owner: 

AUGMENTECH EDUCATION PVT. LTD.
augmotech@gmail.com
<https://www.augmotech.com/>
JAMSHEDPUR, INDIA-832110

25 FLOORS OFFICE BUILDING

WEST HIGH COURT ROAD
MICHIGAN, USA

ISSUE NO.	DELTA	ISSUE DATE	DESCRIPTION
1	1	2022.04.30	ISSUED FOR PERMIT

CURRENT ISSUE

ISSUED FOR PERMIT


CURRENT ISSUE DATE
2022.04.30
DRAWN BY
VR
CHECKED BY
CT
PROJECT NO.
179-64-01

SHEET NAME

BUILDING NORTH ELEVATION

DRAWINGS NO.

A104

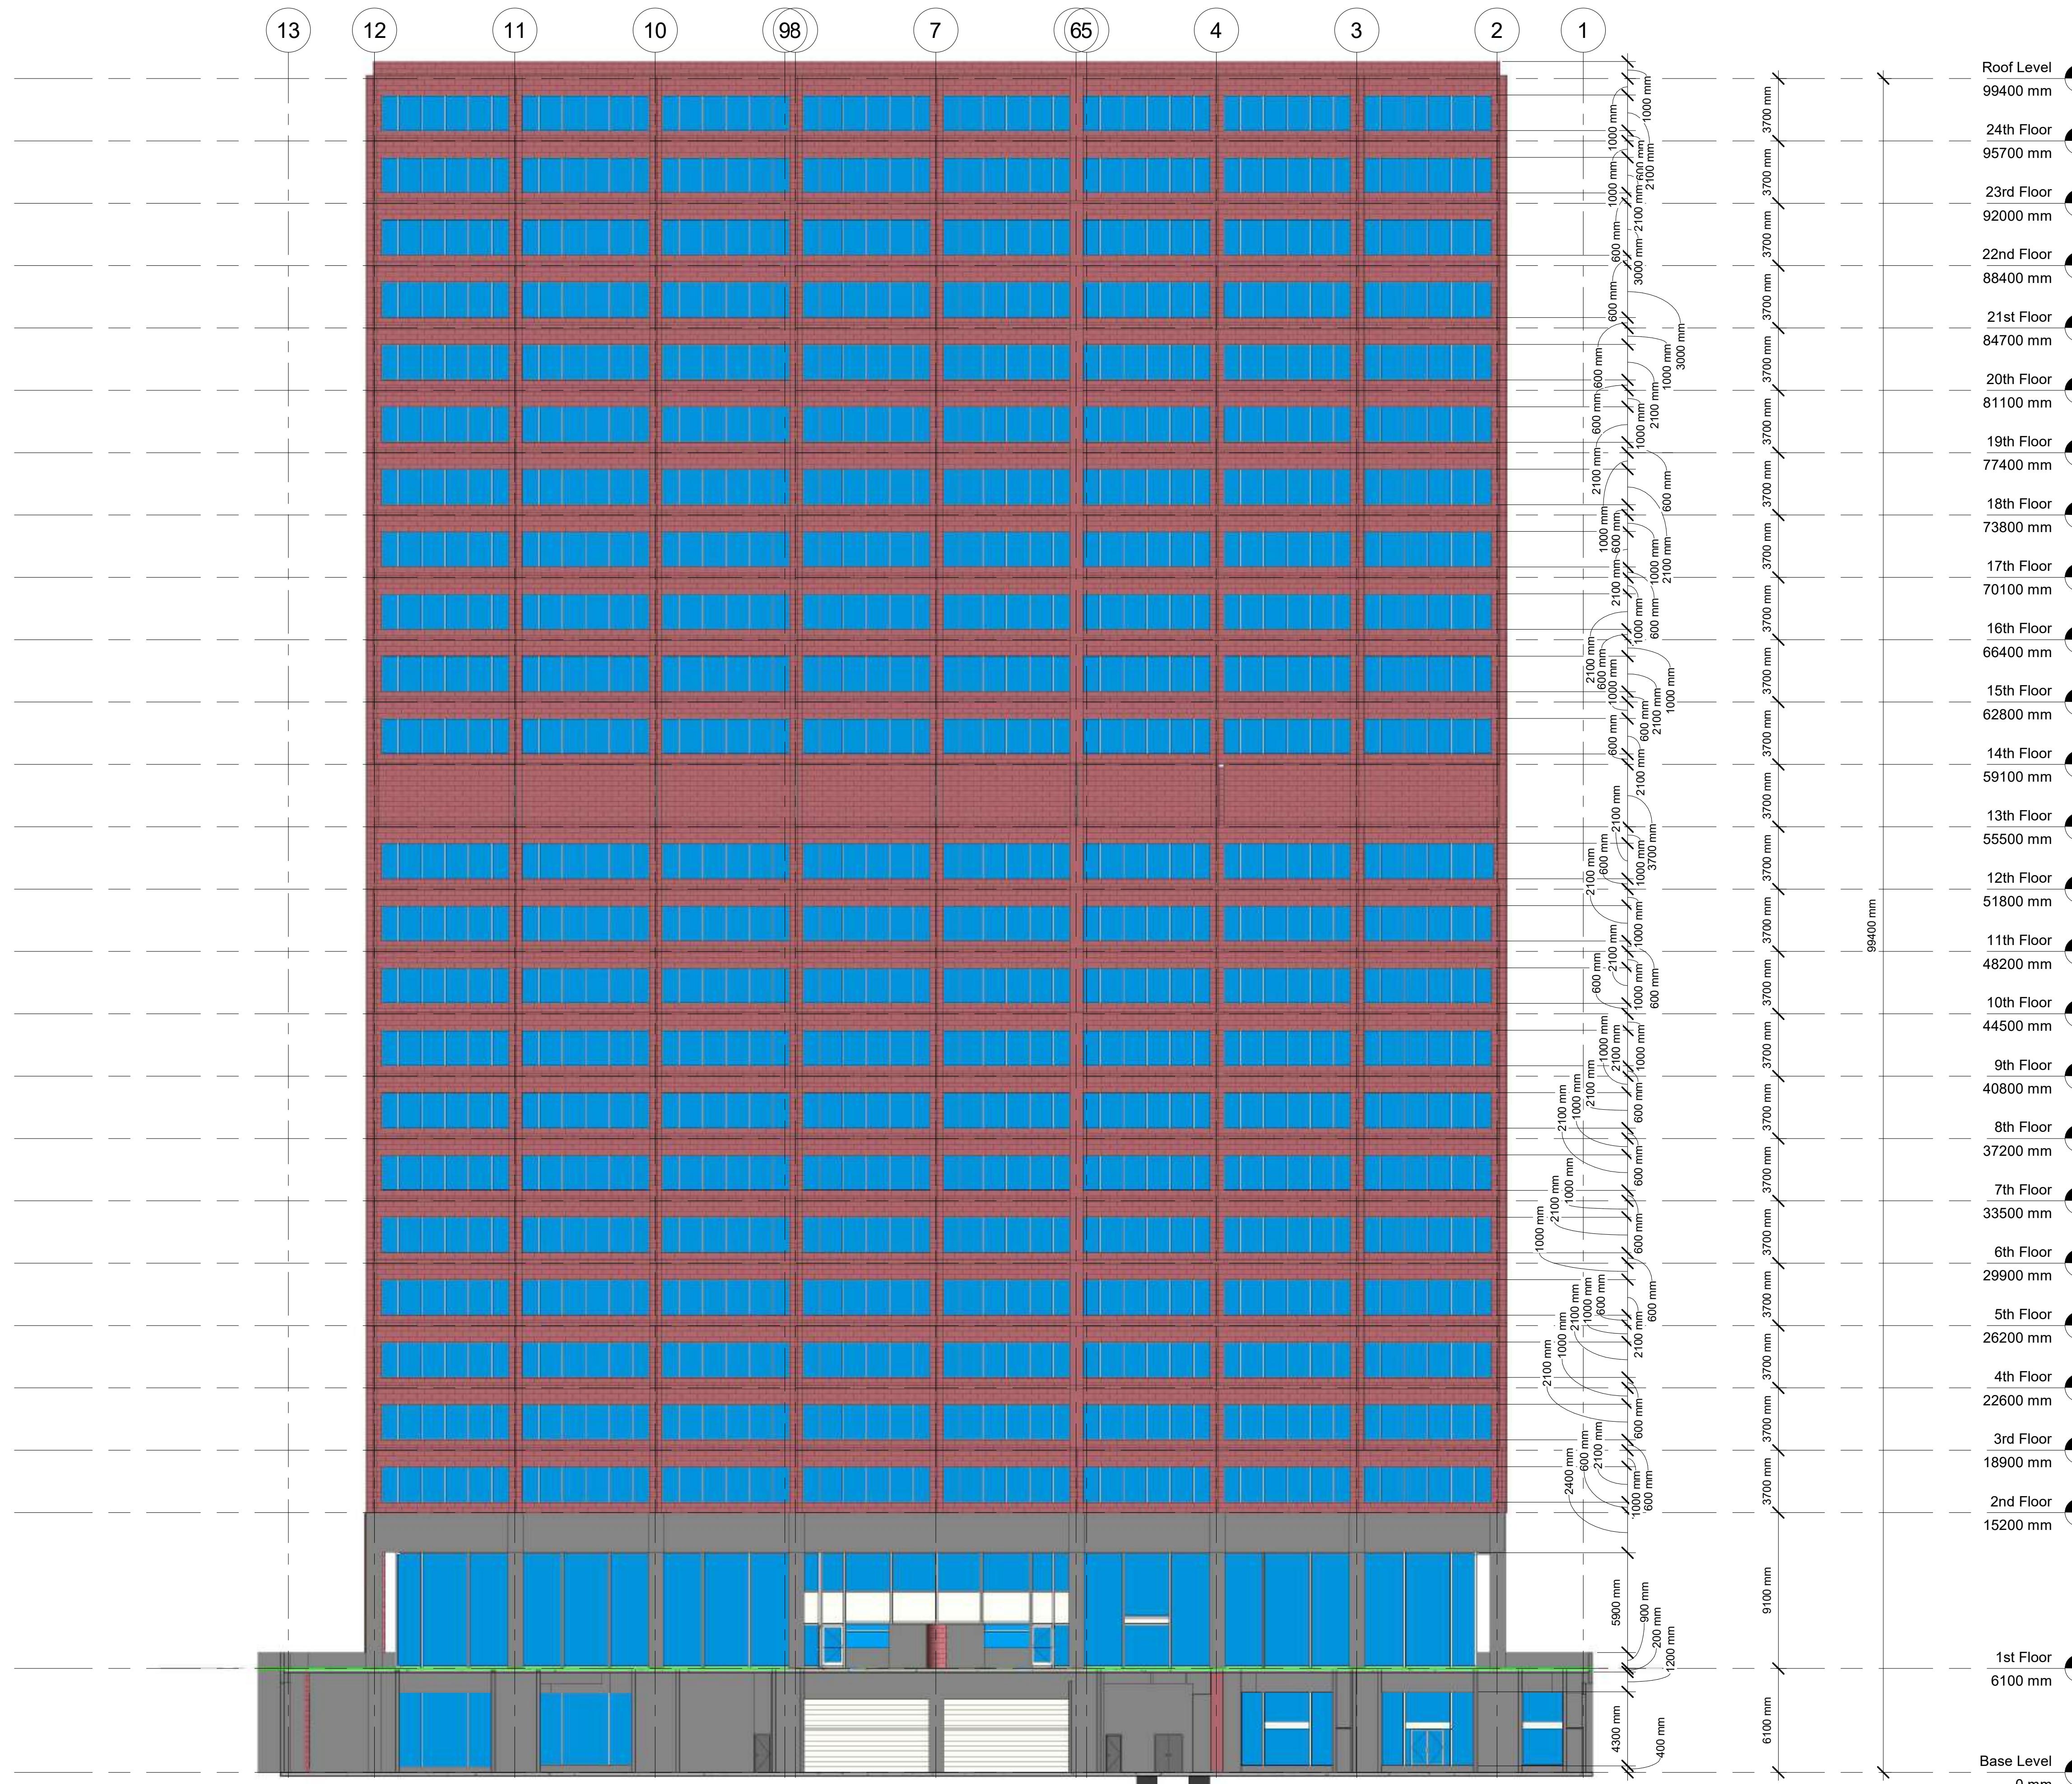


Seal:

DATE: 2022.04.21

Owner:




AUGMENTECH EDUCATION PVT. LTD.
augmotech@gmail.com
<https://www.augmotech.com/>
JAMSHEDPUR, INDIA-832110

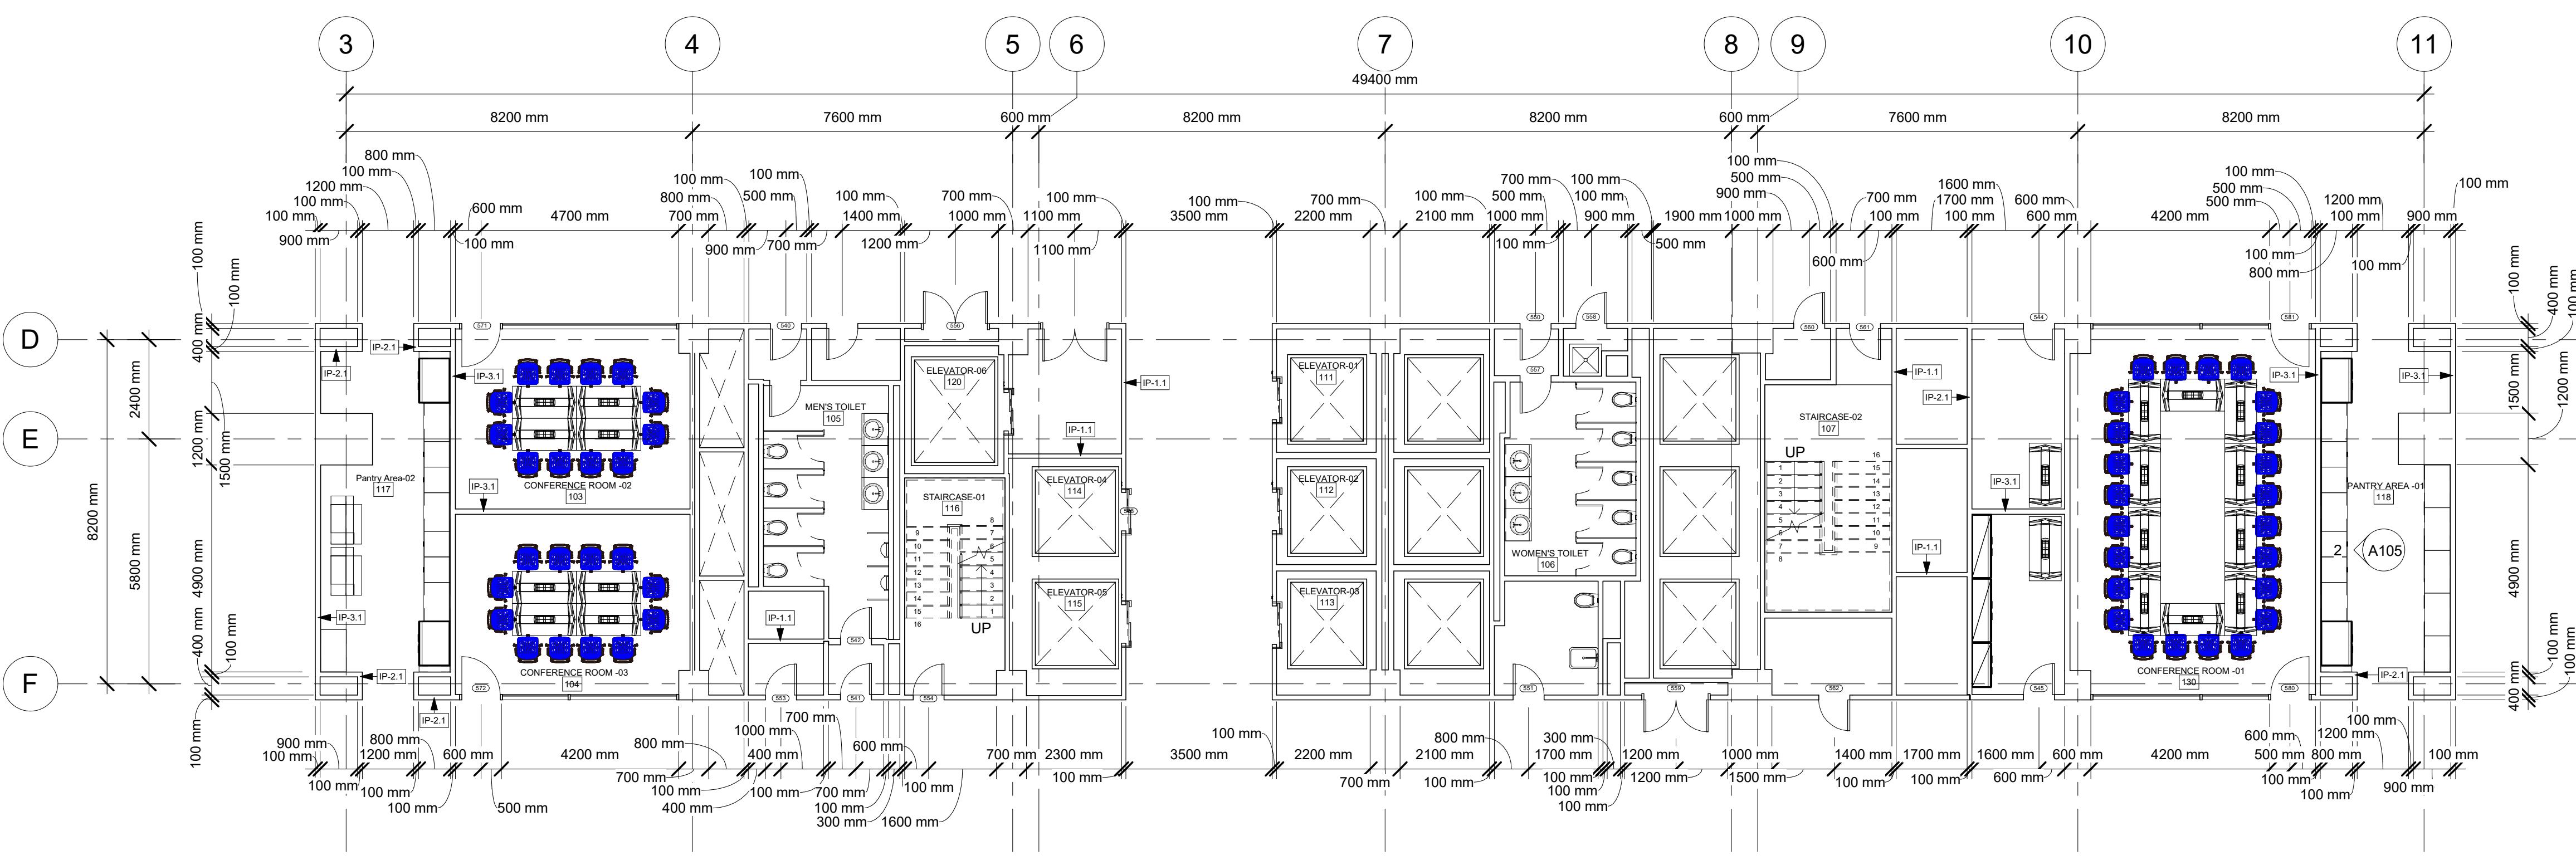

1 Typical Enlarge Plan -01

1 : 100

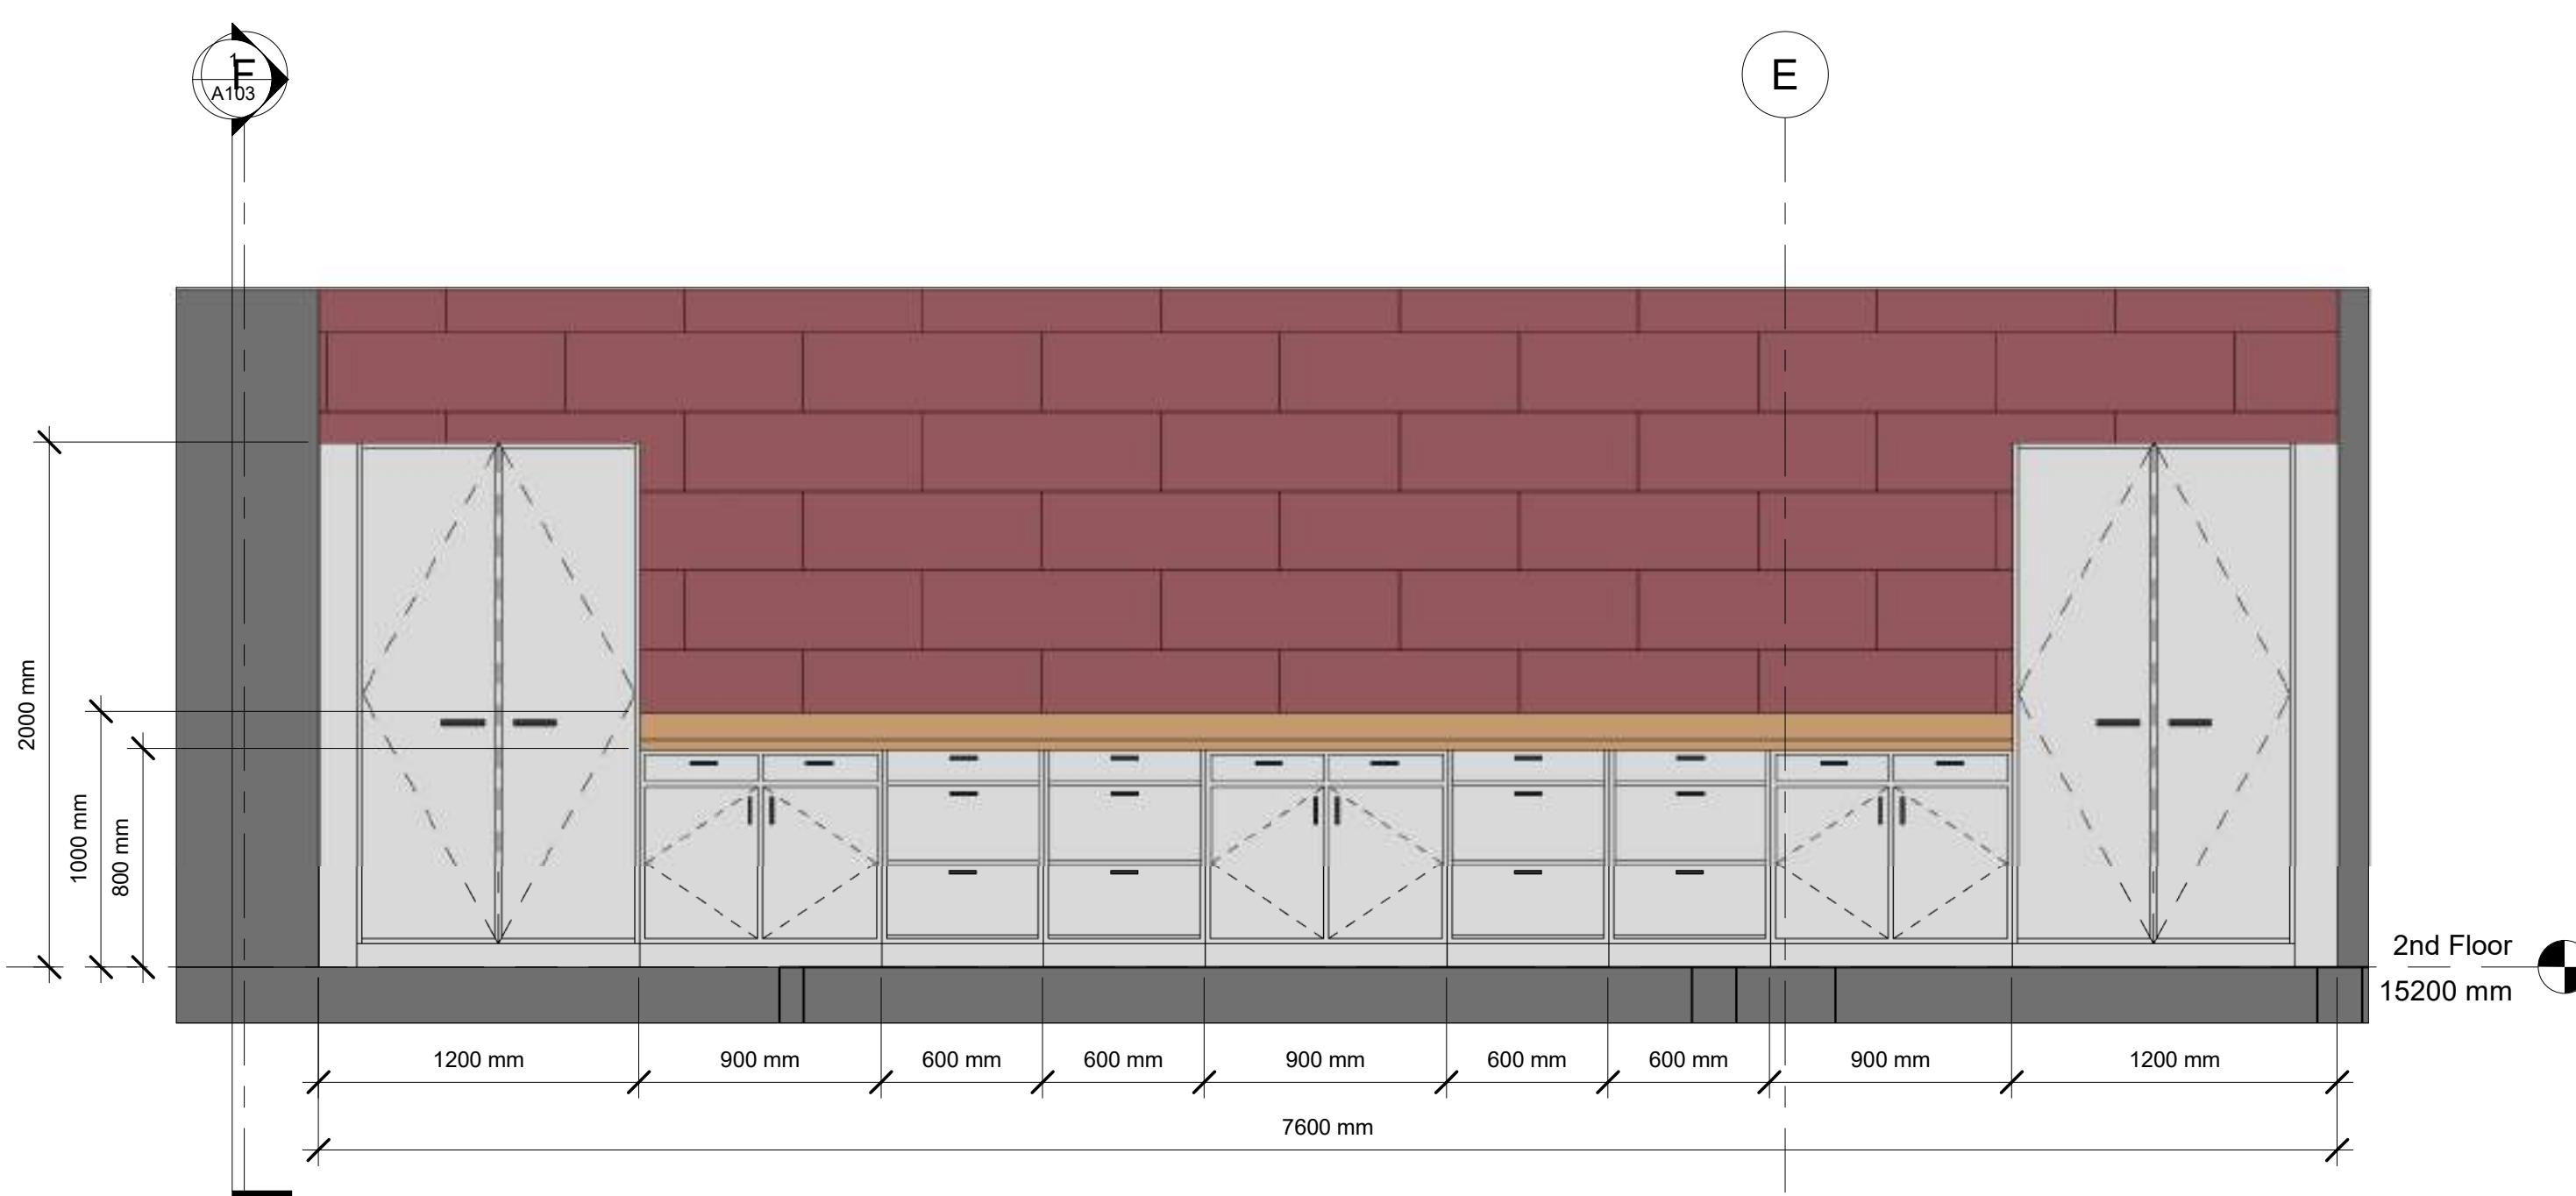

2 Interior Elevation -01

1 : 25

ISSUE NO.	DELTA	ISSUE DATE	DESCRIPTION
1	1	2022.04.30	ISSUED FOR PERMIT

CURRENT ISSUE	
ISSUED FOR PERMIT	
CURRENT ISSUE DATE	2022.04.30
DRAWN BY	VR
CHECKED BY	CT
PROJECT NO.	179-64-01

SHEET NAME

TYPICAL ENLARGE PLAN

DRAWINGS NO.

A105

Door_Schedule				
Family	Type	Width	Height	Count
2_Panel_Bifold_Door_18618	24" x 84"	600 mm	2100 mm	1
Door Single - Hinged + Sidelite-Full	F-3'-0" x 8'-0" + 14" SL	900 mm	2400 mm	3
Door-Bifold_9052	Double Bifold Door 48" x 84"	1200 mm	2100 mm	1
Door-Curtain-Wall-Double-Glass	Door-Curtain-Wall-Double-Glass	2100 mm	2000 mm	2
Door-Double-Flush_Panel	60" x 84"	1500 mm	2100 mm	6
Door-Exterior-Side_Lite-Full Flat Glass-Wood_Clad	12" x 84"	500 mm	2200 mm	24
Door-Opening	72" x 84"	0 mm	0 mm	1
Door-Overhead-Rolling	168" x 168"	7300 mm	4300 mm	2
Door-Passage-Double-Flush	60" x 84"	1500 mm	2100 mm	79
Door-Passage-Single-Flush	33" x 84"	800 mm	2100 mm	38
Door-Passage-Uneven-Flush	50" x 84"	1400 mm	2100 mm	1
Side_opening_Elevatorlift_Door_with_Call_buttons_9478	34	800 mm	2100 mm	156
Single-Flush	29" x 84"	700 mm	2100 mm	532

DATE: 2022.04.21

Owner:



AUGMENTECH EDUCATION PVT. LTD.
augmotech@gmail.com
<https://www.augmotech.com/>
JAMSHEDPUR, INDIA-832110

25 FLOORS OFFICE BUILDING

WEST HIGH COURT ROAD
MICHIGAN, USA

ISSUE NO.	DELTA	ISSUE DATE	DESCRIPTION
1	1	2022.04.30	ISSUED FOR PERMIT

CURRENT ISSUE

ISSUED FOR PERMIT

CURRENT ISSUE DATE
2022.04.30

DRAWN BY
VR

CHECKED BY
CT

PROJECT NO.
179-64-01

SHEET NAME

DOOR SCHEDULE

DRAWINGS NO.

A106